



لمديرية العامة للشؤون الفنيا إدارة إباحات البناء

يعتهد حسب الإباحة الصادرة

يحب الإلتزام بطلاء الواجمات باللون الأبيض فقط يجب على المقاول المنفذ للمشروع والاستشاري المشرف الالتزام بالتنفيذ حسب المخططات المعتمدة والتقيد ببنود الاباحة المشروطة، وبالاشتراطات المحلية والدولية المعتمدة عند التنفيذ.

 يتحول الوكتب الاستشاري الوصوم و المشرف على التنفيذ والمقاول المنفذ –كل في مجال اختصاصه–المسؤولية الكاملة تجاه وجال اختصاصه—الوسؤولية الكاولة تجاه سلامة الوبني وتجاه صحة البيانات الوذكورة بهذا الاعتواد، وصحة البيانات الوذكورة والتصاويم الورفقة وتوافقها وع الأور الوحلي رقم ٢٣/٩٢ والقوانين والتعاويم واشتراطات الرسم الوساحي وضوان استيفاء جويع الموافقات الوطلوبة للوشروع والالتزام بكافة المواصفات والاشتراطات والارشادات المحتودة ون حورة والارتصاص الأختصاص اللوشادات المعتمدة من جميع جمات الاختصاص الأخرى وبما لا يتعارض مع الخرائط المصدقة من هذه

• يلتزم المكتب الاستشاري المشرف والمقاول المنفذ بتوفير الحماية اللازمة للمشروع وسلامة المباني والخدمات المجاورة مع الاخذ بالاعتبار طبيعة التربة والتأثيرات الانشائية

الحوايات اللازوة جمة الوادى قبل الشروع

يجب الالتزام باستخدام اللون الابيض بالواجهات أو التُنسُيق مع المُديرياتُ بالمِناطَق في حالة الرغبة خلاف ذلك. • يجب على المقاول المنفذ للمشروع والاستشاري المشرف الرجوع إلى هذه الادارة قبل تنفيذ الَّمبنى في حالة وجود وشكلة فنية .ت تحول دون البناء حسـب الخرائط المعتمدةِ وفي حالة عدم تطابق الخرائط مع بعضها أو مع الموقع في الطبيعة .

GENERAL NOTES:

1. THESE DRAWINGS ARE THE COPYRIGHT OF MUAMIR DESIGN & ENGINEERING CONSULTANCY LLC & IT SHOULD NOT BE REPRODUCED IN ANY WAY WITHOUT WRITTEN PERMISSION OF TH

2. ALL DRAWINGS TO BE THOROUGHLY CHECKED BY THE CONTRACTOR BEFORE START OF THE WORK. DISCREPANCIES IF ANY SHOULD BE BROUGHT TO THE NOTICE OF THE SUPERVISING CONSULTING ENGINEER FOR CLARIFICATION PRIOR TO ANY WORK.

3. DO NOT SCALE THE DRAWINGS. ONLY WRITTEN DIMENSIONS TO BE FOLLOWED.

4. ALL DIMENSIONS ARE IN MILLIMETERS, UNLESS OTHERWISE INDICATED.

5. ALL DIMENSIONS LEVELS AND/OR HEIGHT INDICATED ON THESE DRAWINGS ARE OF UNFINISHED SURFACES, UNLESS OTHERWISE INDICATED.

6. PLINTH LEVEL TO BE ESTABLISHED AT SITE IN CONSULTATION WITH ARCHITECT, ENGINEER

MINIMUM BEING WHAT IS SHOWN IN THE DRAWINGS. 7. ALL WORKS TO BE CARRIED OUT STRICTLY IN ACCORDANCE WITH THESE DRAWINGS AND

ACCOMPANYING DOCUMENTS. CHANGES, IF ANY, WOULD BE INSTRUCTED AND/OR APPROVED BY THE ARCHITECT/ ENGINEER.

8. WHENEVER PROPRIETARY MATERIALS ARE SPECIFIED, THEY SHALL BE EMPLOYED STRICTLY IN ACCORDANCE WITH THE MANUFACTURERS RECOMMENDATIONS.

9. ALL MATERIALS USED SHALL COMPLY WITH RELEVANT OMAN STANDARDS. IN ABSENCE OF OMAN STANDARDS, IT SHALL COMPLY WITH A RELEVANT OR EQUIVALENT INTERNATIONAL STANDARDS. SAMPLES/TRADE LITERATURE SHALL BE SUBMITTED TO THE CONSULTING ENGINEER FOR THEIR APPROVAL BEFORE IMPLYING ANY MATERIAL ON SITE.

10. ANTI-TERMITE TREATMENT SHALL BE CARRIED OUT BY SPECIALIZED AGENCY APPROVED BY THE CONSULTING ENGINEER AND THE GOVERNMENT OF SULTANATE OF OMAN.

11. WATERPROOFING SHALL BE CARRIED OUT BY SPECIALIZED AGENCY APPROVED BY THE CONSULTING ENGINEER AND THE GOVERNMENT OF SULTANATE OF OMAN.

12. ALL SUNKEN FLOOR SLABS IN BATHS/TOILETS/KITCHENS/PANTRY ETC. ON FIRST/TERRACE AND ANY OTHER FLOOR SHALL BE TREATED WITH APPROVED WATERPROOFING PRIOR TO LAYING OF PIPES AND FILLING MATERIALS.

13. ALL DRAINAGE DUCTS TO BE COVERED BY GRC. APPROVED BY THE CONSULTING ENGINEER AND CLIENT.

- 1				
	01	ISSUED FOR APPROVAL	06.01.2016	AJ
	00	ISSUED FOR APPROVAL	28-12-2015	AJ
	NO.	DESCRIPTION	DATE	CHECKED

CONSULTANT: Muamix DESIGN AND ENGINEERING CONSULTANCY LLC.

HEAD OFFICE: BUILDING NO. 1667, WAY NO. 122, AL- WATTAYAH, BAUSHER, SULTANATE OF OMAN P.O.BOX 3271, P.C 112 RUWI. TEL: +968 24 560 407 / +968 24 560 408, FAX: +968 24 560 417 EMAIL: info@muamir.com, WEBSITE: www.muamir.com CR 01/40214/5

BRANCHES: NIZWA: P.O.BOX 743, P.C 611, TEL: +968 25 410 456 SOHAR: P.O.BOX 524, P.C 311, TEL: +968 26 841 843 IBRI: P.O.BOX 529, P.C 511, TEL: +968 25 690 458


Mr. LOUAI FATHI SAID AYEDEH Mr. MAHIR MOHAMED NASSER AL LAMKI

PROPOSED RESIDENTIAL PRIVATE TWIN VILLA

NO. OF FLOORS: PLOT: LOCATION: 412 /Phase - 1 AL SEEB / AL MAWALEH N. RESIDENTIAL ARCHITECTURAL

FIRST FLOOR PLAN

APPROVED BY: DATE: SCALE: ISSUED FOR: DRAWN BY: CHECKED BY: JAN-2016 | 1:100 - A1 | M. MUNICIPALITY RT FILE NO: PROJECT NO: DRAWING NO: A-110 3876

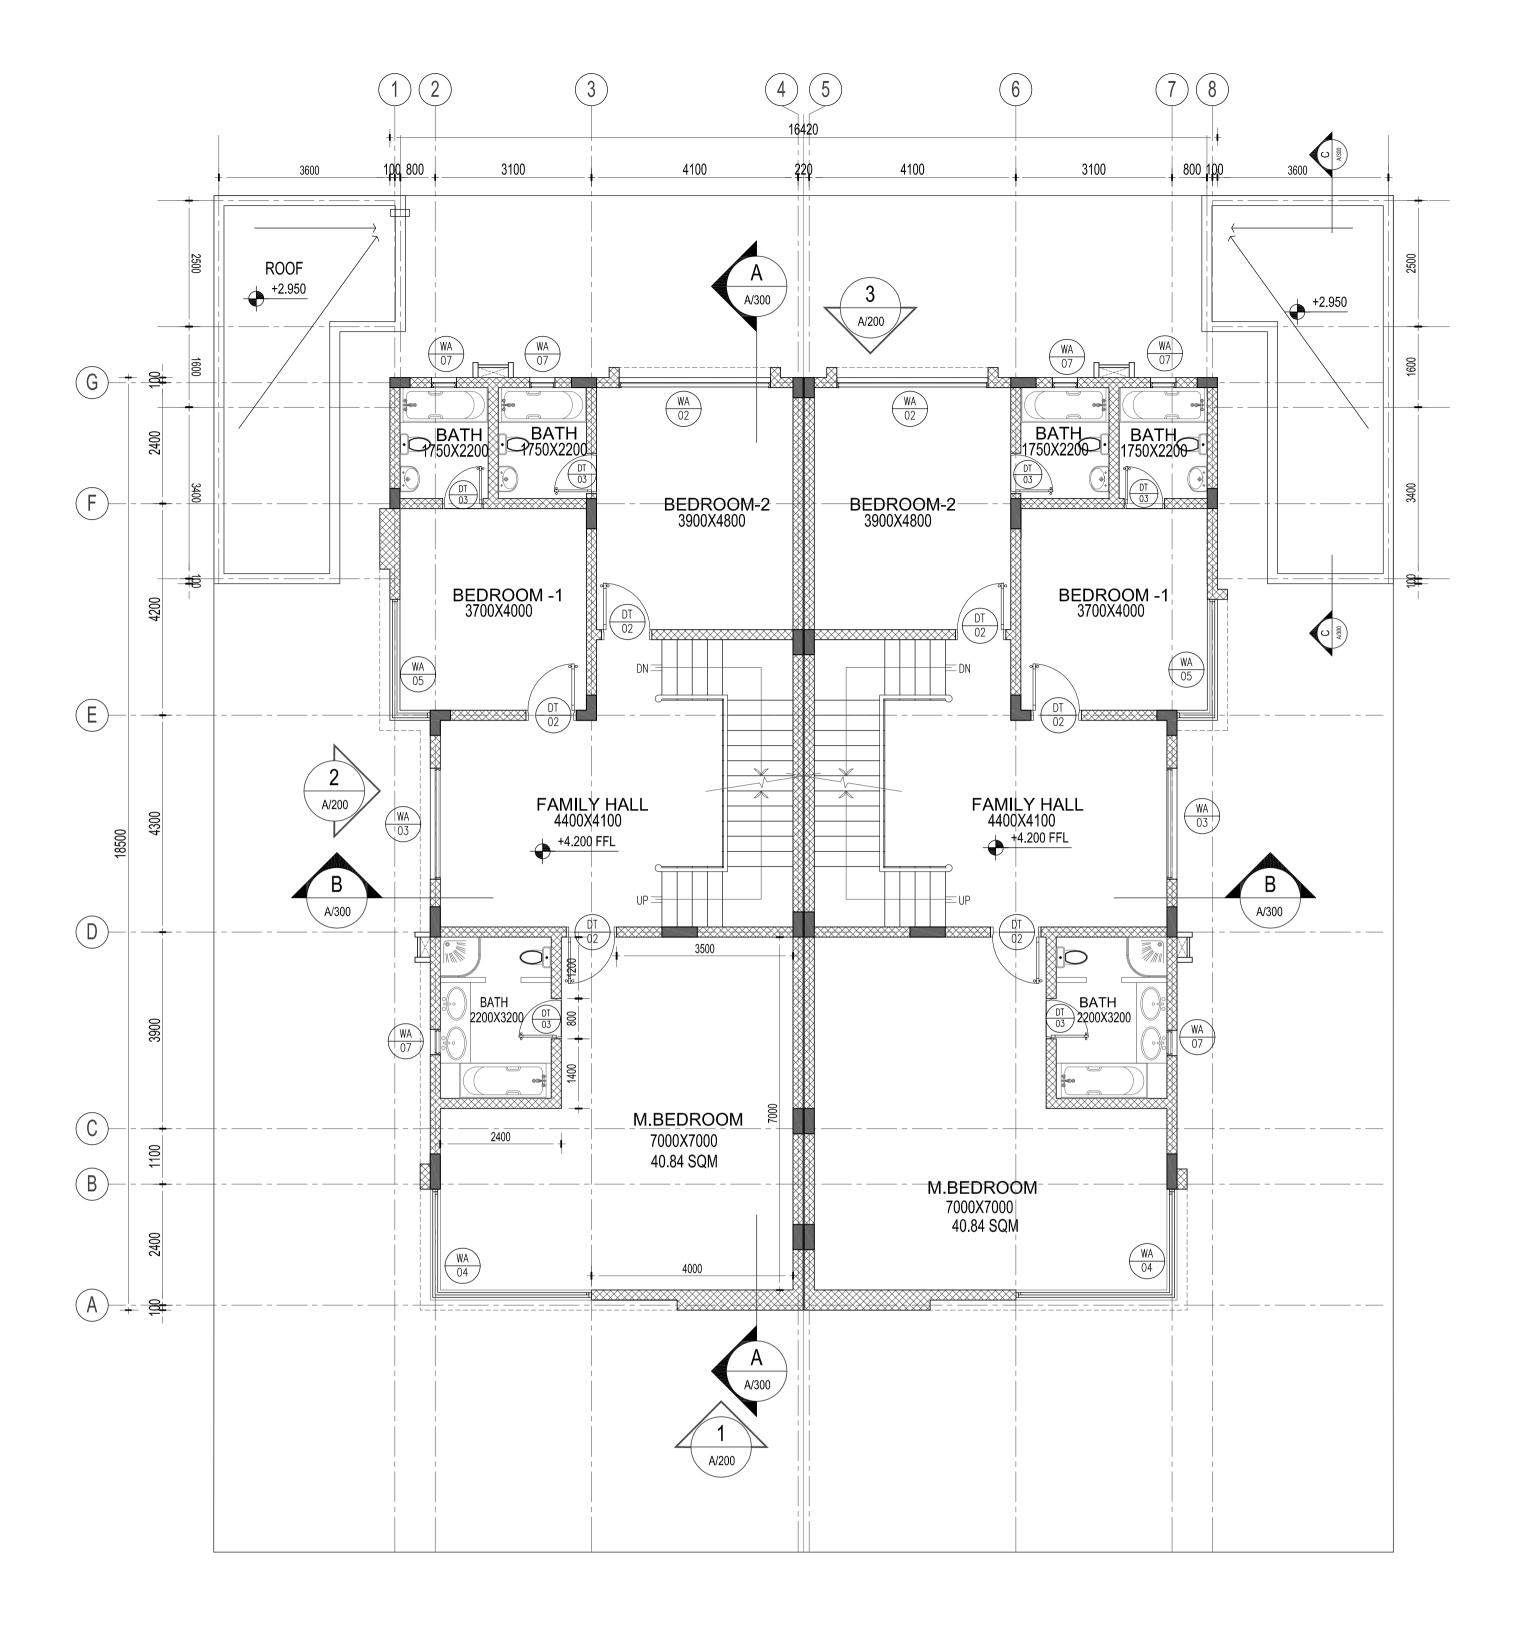

FIRST FLOOR PLAN

SCALE 1:75

APPROVED By shamsa alabri at 8:53 am, Jan 07, 2016